
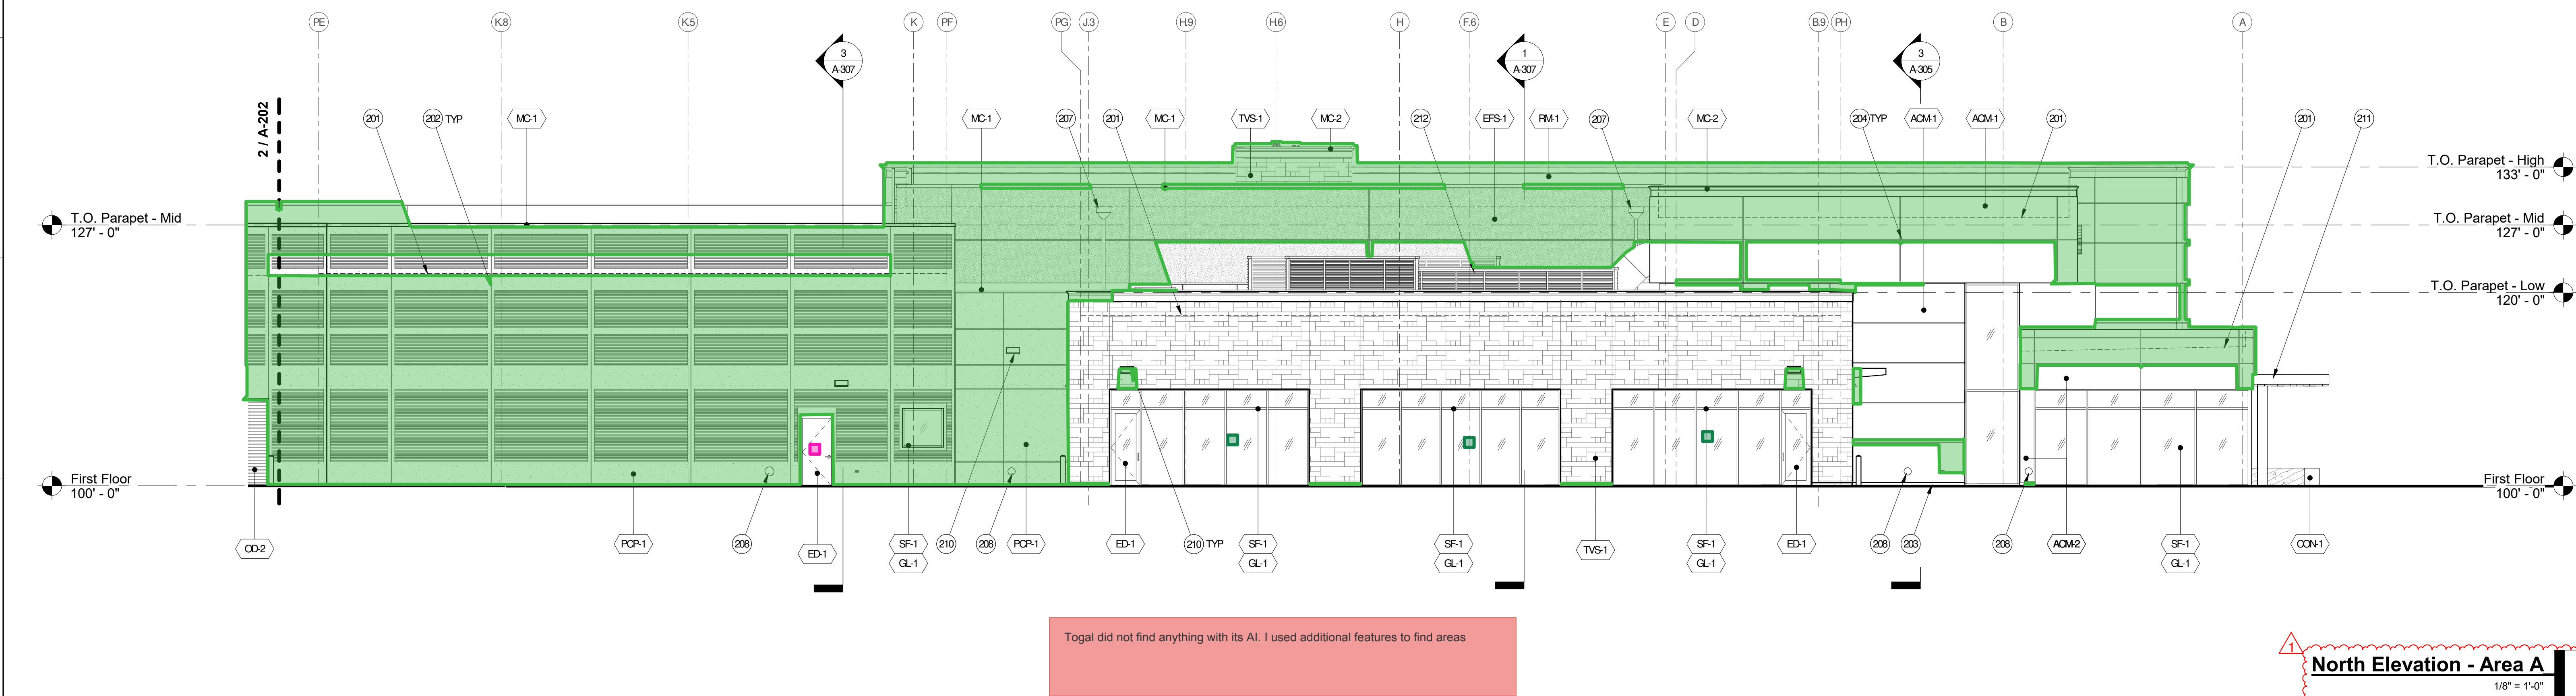
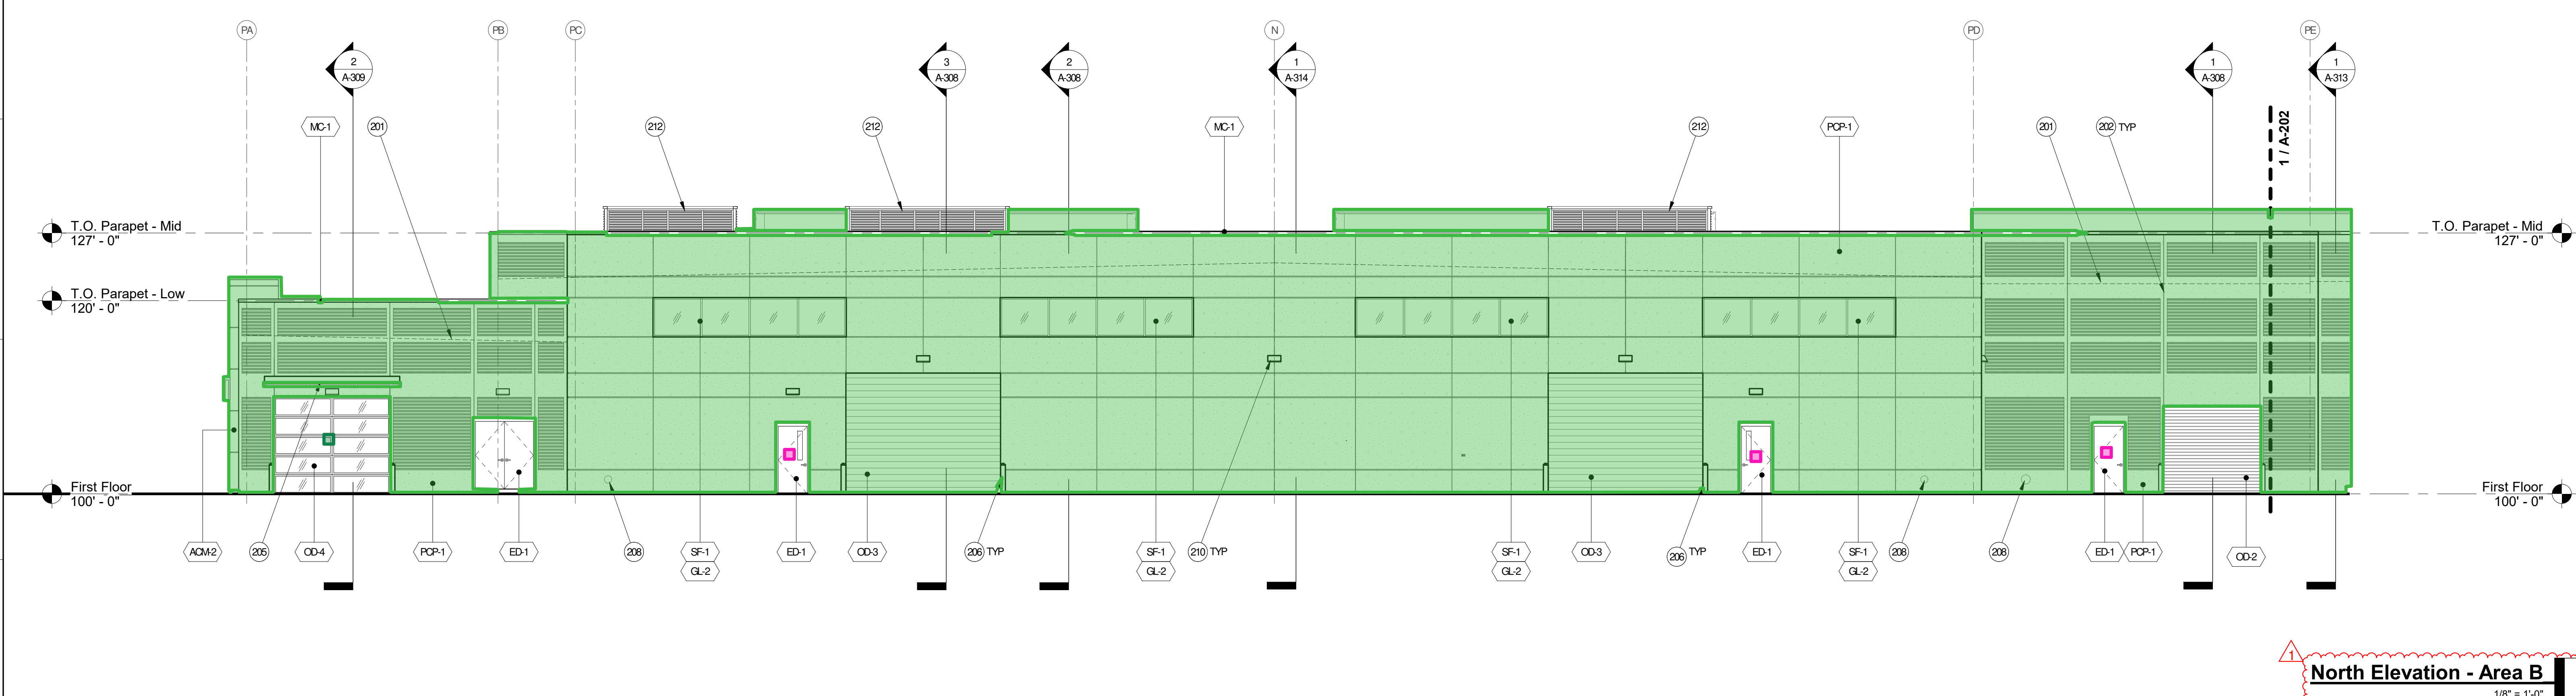


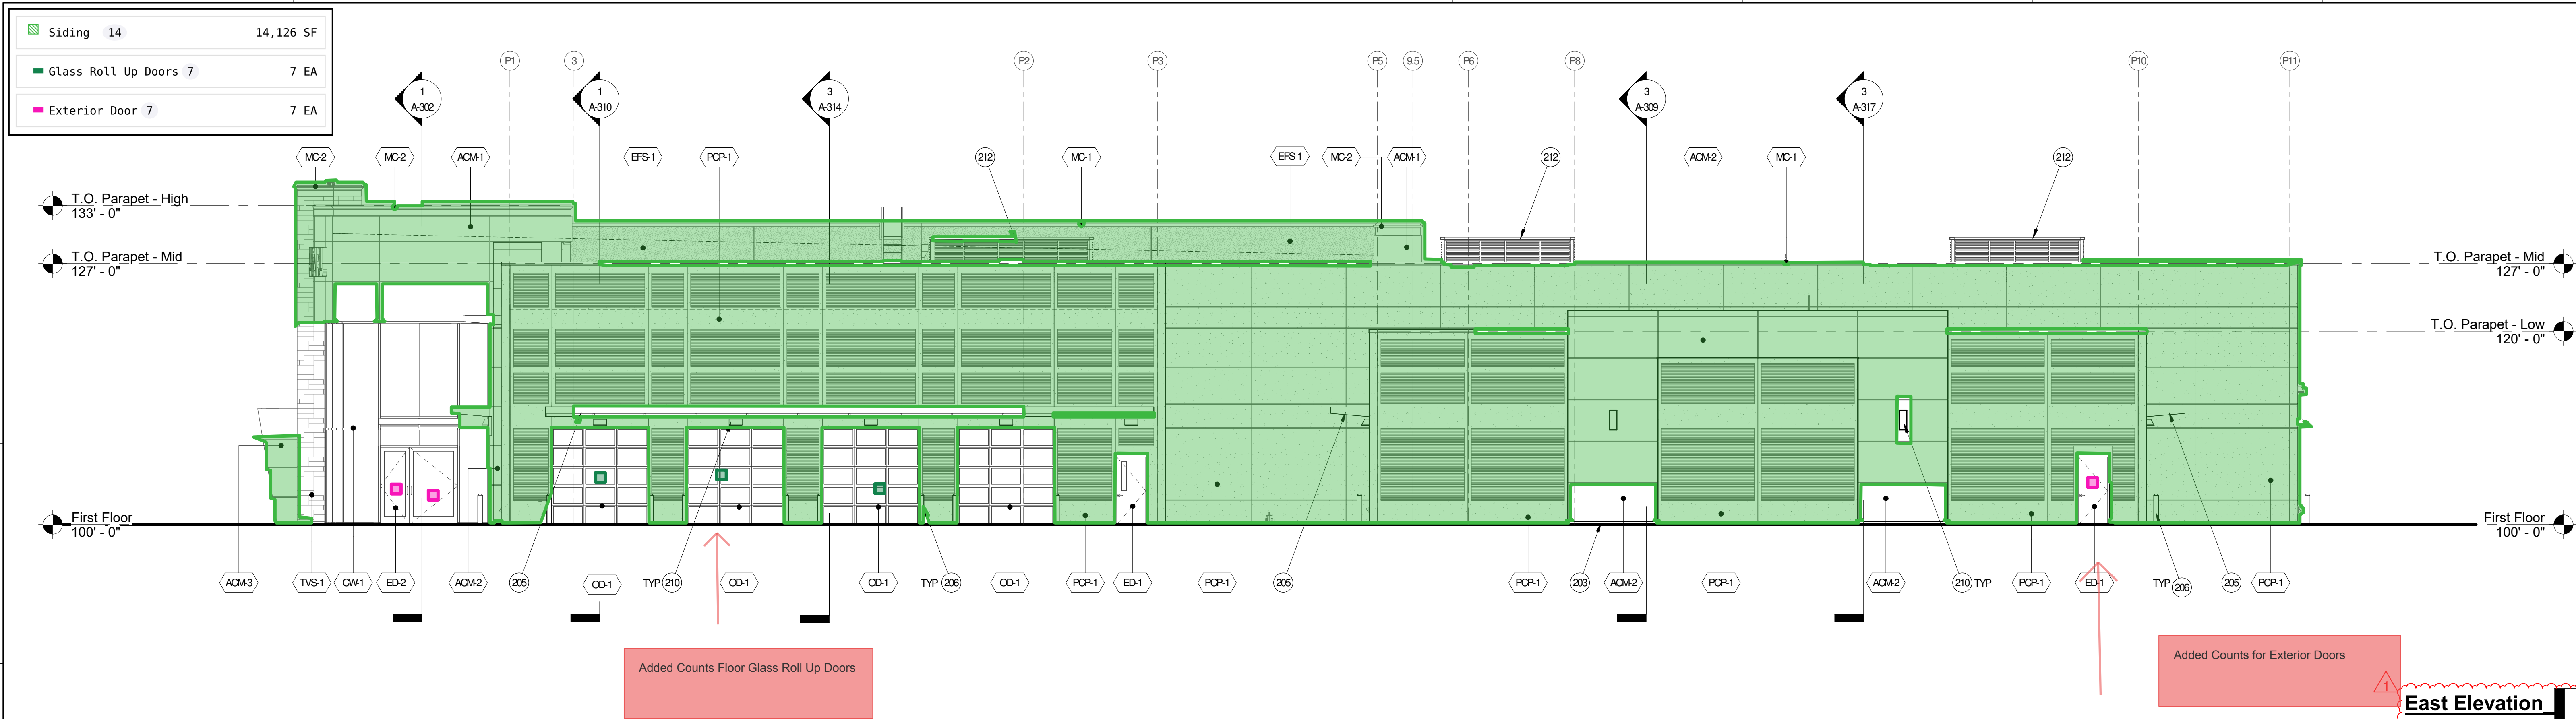

MATERIALS	
ACM1	ALUMINUM COMPOSITE PANEL WALL SYSTEM MANUFACTURER: ALPOLC COLOR: BSK SILVER
ACM2	ALUMINUM COMPOSITE PANEL WALL SYSTEM MANUFACTURER: ALPOLC COLOR: MCAMS GREY
ACM3	ALUMINUM COMPOSITE PANEL WALL SYSTEM MANUFACTURER: ALPOLC COLOR: PIGMENTO GZZ GREY
CON1	ARCHITECTURAL CAST IN PLACE CONCRETE SEAT WALL WITH FORMLINER
OW1	ALUMINUM CURTAIN WALL SYSTEM MANUFACTURER: KAWNEER 1600 SYSTEM2 COLOR FINISH: CLEAR AND OZED (SEE FRAME ELEVATIONS)
ED1	FLUSH HOLLOW CORE STEEL DOOR WITH HIGH PERFORMANCE COATING COLOR: TBO (SEE DOOR SCHEDULE)
ED2	ALUMINUM GLASS STOREFRONT DOORS MANUFACTURER: KAWNEER WIDE STILE COLOR: CLEAR AND OZED (SEE DOOR SCHEDULE)
EFS-1	EXTERIOR INSULATION FINISH SYSTEM MANUFACTURER: STO CORPORATION FINISH: FINE TEXTURE COLOR: MATCH ACM1
GL-1	CLEAR INSULATED LOWE GLAZING
GL-2	TRANSLUCENT INSULATED LOWE GLAZING
MC-1	PREFINISHED METAL CORING AND SHEET METAL FLASHING MANUFACTURER: BERRIDGE MFG COLOR: LEAD COTE
MC-2	PREFINISHED ALUMINUM CORING ASSEMBLY WITH TOP CAP AND CUSTOM FABRICA VERTICAL FACE TO BE PWS 281C REMAINER OF METAL TO BE SILVER METALLIC FINISH RE: DETAIL 14/A-202
OD-1	ALUMINUM FRAME GLASS OVERHEAD DOOR COLOR FINISH: CLEAR AND OZED (SEE DOOR SCHEDULE - OCPN)
OD-2	INSULATED COILING STEEL OVERHEAD DOOR FINISH: FACTORY FINISH COLOR: MATCH EXTERIOR WALL DOORS (SEE DOOR SCHEDULE - OPCS)
OD-3	ALUMINUM AND CLEAR ACRYLIC POLYCARBONATE HIGH SPEED ROLLING DOOR RE: DOOR SCHEDULE (OVC)
OD-4	ALUMINUM FRAME OVERHEAD DOOR WITH POLYCARBONATE GLAZING COLOR FINISH: CLEAR AND OZED RE: DOOR SCHEDULE (CPPA)
PCP-1	PREFAB INTEGRAL COLOR CONCRETE WALL PANELS WITH AGGREGATE FINISH (LIGHT AGGREGATE EXPOSURE) AND FORMLINER PROFILE PATTERN FITZGERALD 1407 FLUTED FB RE: A-107 & A-108
RM1	ROOF MEMBRANE AT BACK SIDE OF PARAPET COLOR: GRAY
SF-1	ALUMINUM STOREFRONT SYSTEM MANUFACTURER: KAWNEER TRIFAB VERSAGLAZE 451-T COLOR: CLEAR AND OZED (SEE FRAME ELEVATIONS)
TVS-1	THIN VENEER SLATE MANUFACTURER: CAMPA SLATE PRODUCTS COLOR: SHADOW GREY

KEYNOTES	
201	LINE OF ROOF BEYOND PARAPET
202	PREFAB PANEL JOINT WITH SEALANT COLOR: TBO
203	CAST IN PLACE CONCRETE WALL CURB WITH TEXTURED ACRYLIC COATING COLOR: TBO RE: A-109
204	ACM PANEL JOINT REVEAL
205	PREFABRICATED OPEN LOUVERED ALUMINUM CANOPY RE: WALL SECTIONS
206	6" HD GALVANIZED CONCRETE FILLED STEEL PIPE BOLLARD WITH HP COATING COLOR: TBO
207	THRU WALL SCUPPER WITH PREFINISHED METAL CONDUCTOR HEAD AND DOWNSPOUT, COLOR: LEAD COTE (SEE WALL SECTIONS)
208	ROOF DRAIN OVERFLOW DISCHARGE RE: PLUMBING
209	INTERNALLY ILLUMINATED BUILDING MOUNTED SCORGE BY OWNER RE: ELECTRICAL
210	WALL MOUNTED EXTERIOR LIGHTING RE: ELECTRICAL
211	PREFINISHED ALUMINUM PLANK CANOPY SYSTEM MANUFACTURER: AWDEX COLOR: CLEAR AND OZED FRAMING, WOOD GRAIN POWDER COAT PLANKS
212	PREFINISHED PLASTIC LOUVERED SCREEN WALL DIRECT MOUNTED TO ROOF TOP UNITS COLOR: TBO

SAI
SLAGGIE ARCHITECTS, INC. © 2022
Kansas City, Missouri • Omaha, Nebraska
888.756.1656
slaggie.com

CHARLES W. KELLER
LICENSED
5273
ARCHITECT

Subaru of Olathe
New Automotive Dealership and Service Center
Baxter Automotive Group
119th and Renner Road
Olathe, KS

Revisions:
1. Bldg. Add. 01 03/23/2022

Project #: 210301

Construction Documents
08 March 2022

EXTERIOR ELEVATIONS
A-202