


Total areas		
 Footprint	1	733 SF
 Net area	13	617 SF
 Doors area	1	1 SF
 Gross area	12	664 SF
 Gross Internal Area (GIA)		12590 SF
Total lines		
 Doors centerline	1	2 FT
 Wall centerline	53	257 FT
 Wall Perimeter	14	384 FT
Total counts		
 Single Swing Door	14	14 EA

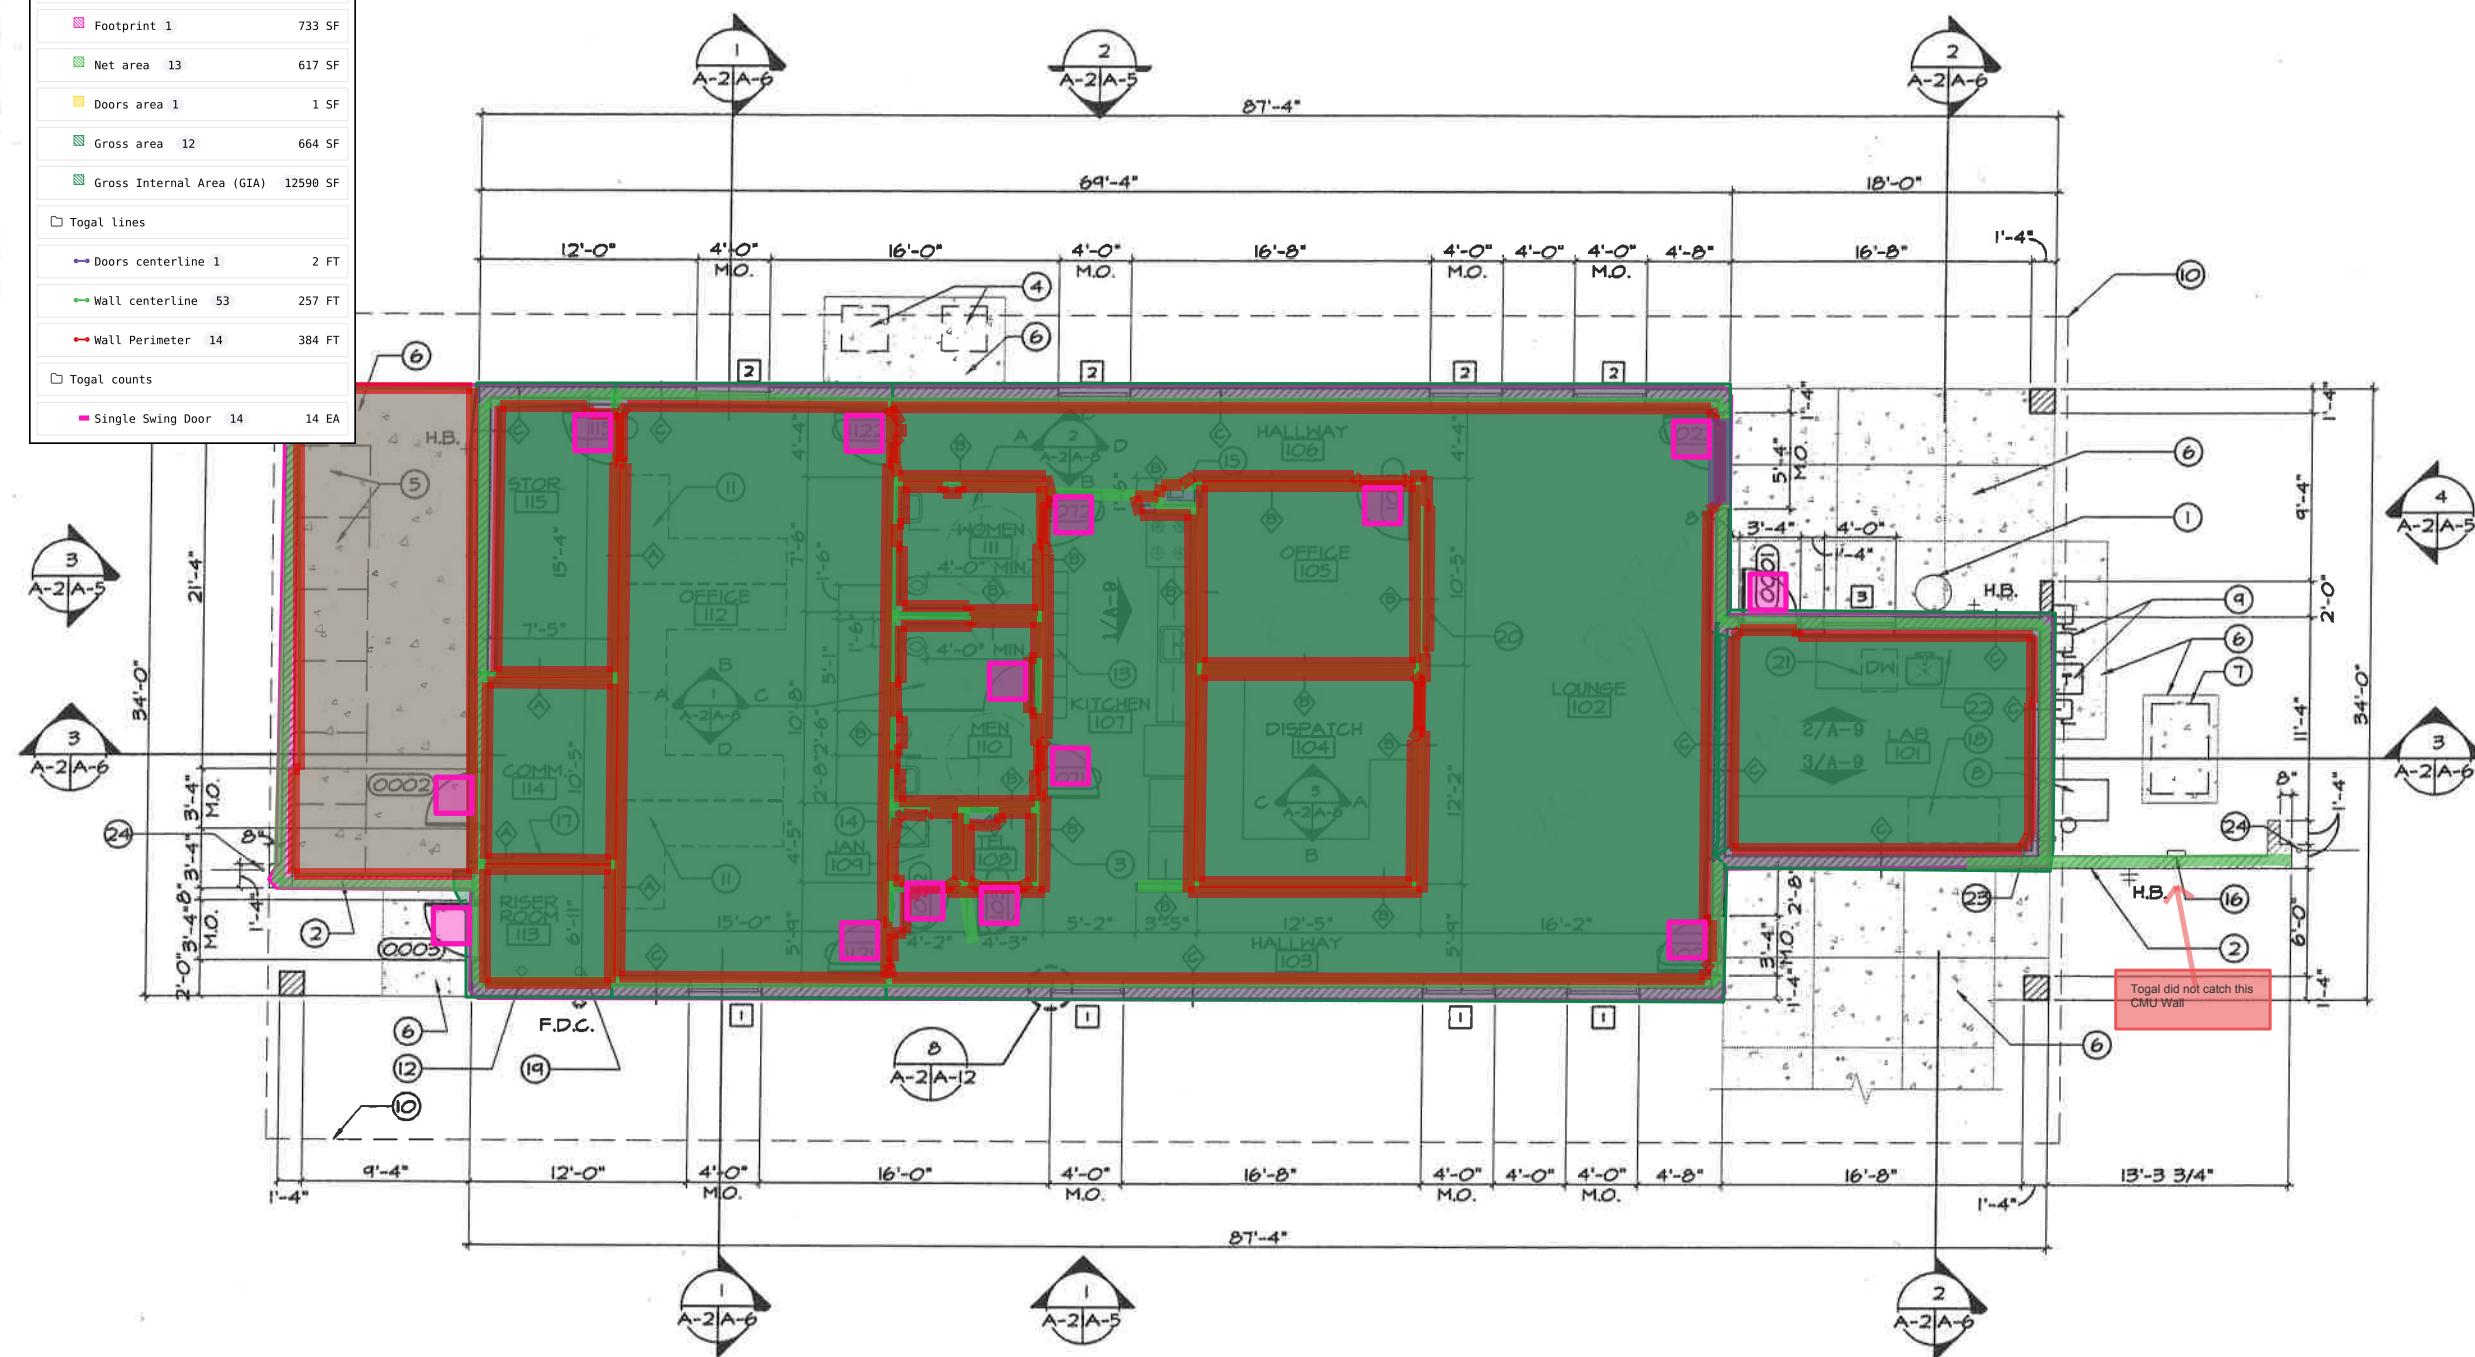

- ## FLOOR PLAN KEY NOTES
- ① OUTDOOR SHOWER AND EYEWASH
 - ② CMU SCREEN WALL- SEE ELEVATIONS FOR HEIGHT
 - ③ ELECTRICAL PANELS FLUSH MOUNTED IN 6" STUD WALL
 - ④ GROUND MOUNTED HEAT PUMP UNITS- REFER TO MECHANICAL DRAWINGS
 - ⑤ OUTDOOR PALLET RACK STORAGE
 - ⑥ CONCRETE PAD / WALK
 - ⑦ GROUND MOUNTED CONDENSING UNIT- REFER TO MECHANICAL DRAWINGS
 - ⑧ WALL MOUNTED EXHAUST FAN- REFER TO MECHANICAL DRAWINGS
 - ⑨ ELECTRICAL SERVICE- REFER TO ELECTRICAL DRAWINGS
 - ⑩ LINE OF ROOF OVERHANGS
 - ⑪ SYSTEMS FURNITURE (N.I.C.)
 - ⑫ DOMESTIC WATER RISER- REFER TO PLUMBING DRAWINGS
 - ⑬ LOCKERS- REFER TO SPECIFICATIONS
 - ⑭ FLOOR MOP SINK WITH 20 GAL. WATER HEATER MOUNTED ABOVE- REFER TO PLUMBING DRAWINGS
 - ⑮ ELECTRIC DRINKING FOUNTAIN
 - ⑯ IRRIGATION CONTROLLER
 - ⑰ TELEPHONE MOUNTING BOARD
 - ⑱ 5' LONG EXHAUST HOOD
 - ⑲ FIRE SPRINKLER RISER
 - 20 BULLETIN BOARD (SUPPLIED BY OWNER, INSTALLED BY CONTRACTOR)
 - 21 DISHWASHER (SUPPLIED BY OWNER, INSTALLED BY CONTRACTOR)
 - 22 COUNTER MOUNTED EYEWASH
 - 23 1" SLEEVE THRU WALL FOR FUEL DRAIN @ 30" A.F.F.
 - 24 SECURITY FENCE- 2"Ø SCHEDULE 40 PIPE IN CONCRETE FOOTING, REFER TO DETAIL 9/A-10. CENTER PIPE 1'-0" BACK FROM FACE OF MASONRY WALL

DEPARTMENT OF THE NAVY SAN DIEGO SOUTHWEST DIVISION NAVAL FACILITIES NAVAL FACILITIES ENGINEERING COMMAND CALIFORNIA		SUBMITTED: DESIGN: DRAWN: CHECKED: FP:		SATISFACTORY TO: FAC MANG. OFFICER: DIRECTOR OF ENG.: SIV DW FOR COMMANDER NAVFAC		DATE DATE DATE DATE		REVISIONS APPROVED DATE PREP. BY DESCRIPTION SYMBOL	
SIZE D IF SHEET IS LESS THAN 22" X 34" IT IS A REDUCED PRINT - SCALE REDUCED ACCORDINGLY		FLOOR PLAN							
PWO. NO.		PROJECT LOCATION							
SPEC.		CONSTR. CONTRACT NO.							
SHEET 14 OF		NAVFAC DRAWING NO.							
A-2									

 **1** **FLOOR PLAN**
SCALE: 3/16" = 1'-0"

WALL LEGEND		
TYPE	DETAIL	DESCRIPTION
		EXTERIOR 8" CMU WALL
	 2/A-II	INTERIOR PARTITION- 5/8" TYPE 'X' GYP. BD. BOTH SIDES 3-5/8" METAL STUD FRAMING, EXTEND TO ROOF STRUCTURE. PROVIDE R-II BATT INSULATION.
	 3/A-II	INTERIOR PARTITION- 5/8" TYPE 'X' GYP. BD. BOTH SIDES 3-5/8" METAL STUD FRAMING, EXTEND WALL TO 9'-6" A.F.F.. PROVIDE R-II BATT INSULATION.
	 4/A-II	INTERIOR PARTITION- FURR OUT CMU WALL W/ 5/8" TYPE 'X' GYP. BD. OVER 3-5/8" METAL STUD FRAMING. PROVIDE SPRAY-ON INSULATION. FRAMING AND INSULATION TO EXTEND TO BOTTOM OF ROOF TRUSSES. PROVIDE TYPE W.R. GYP. BD. AT RESTROOM SIDE OF INTERIOR PARTITIONS

100% SUBMITTAL

